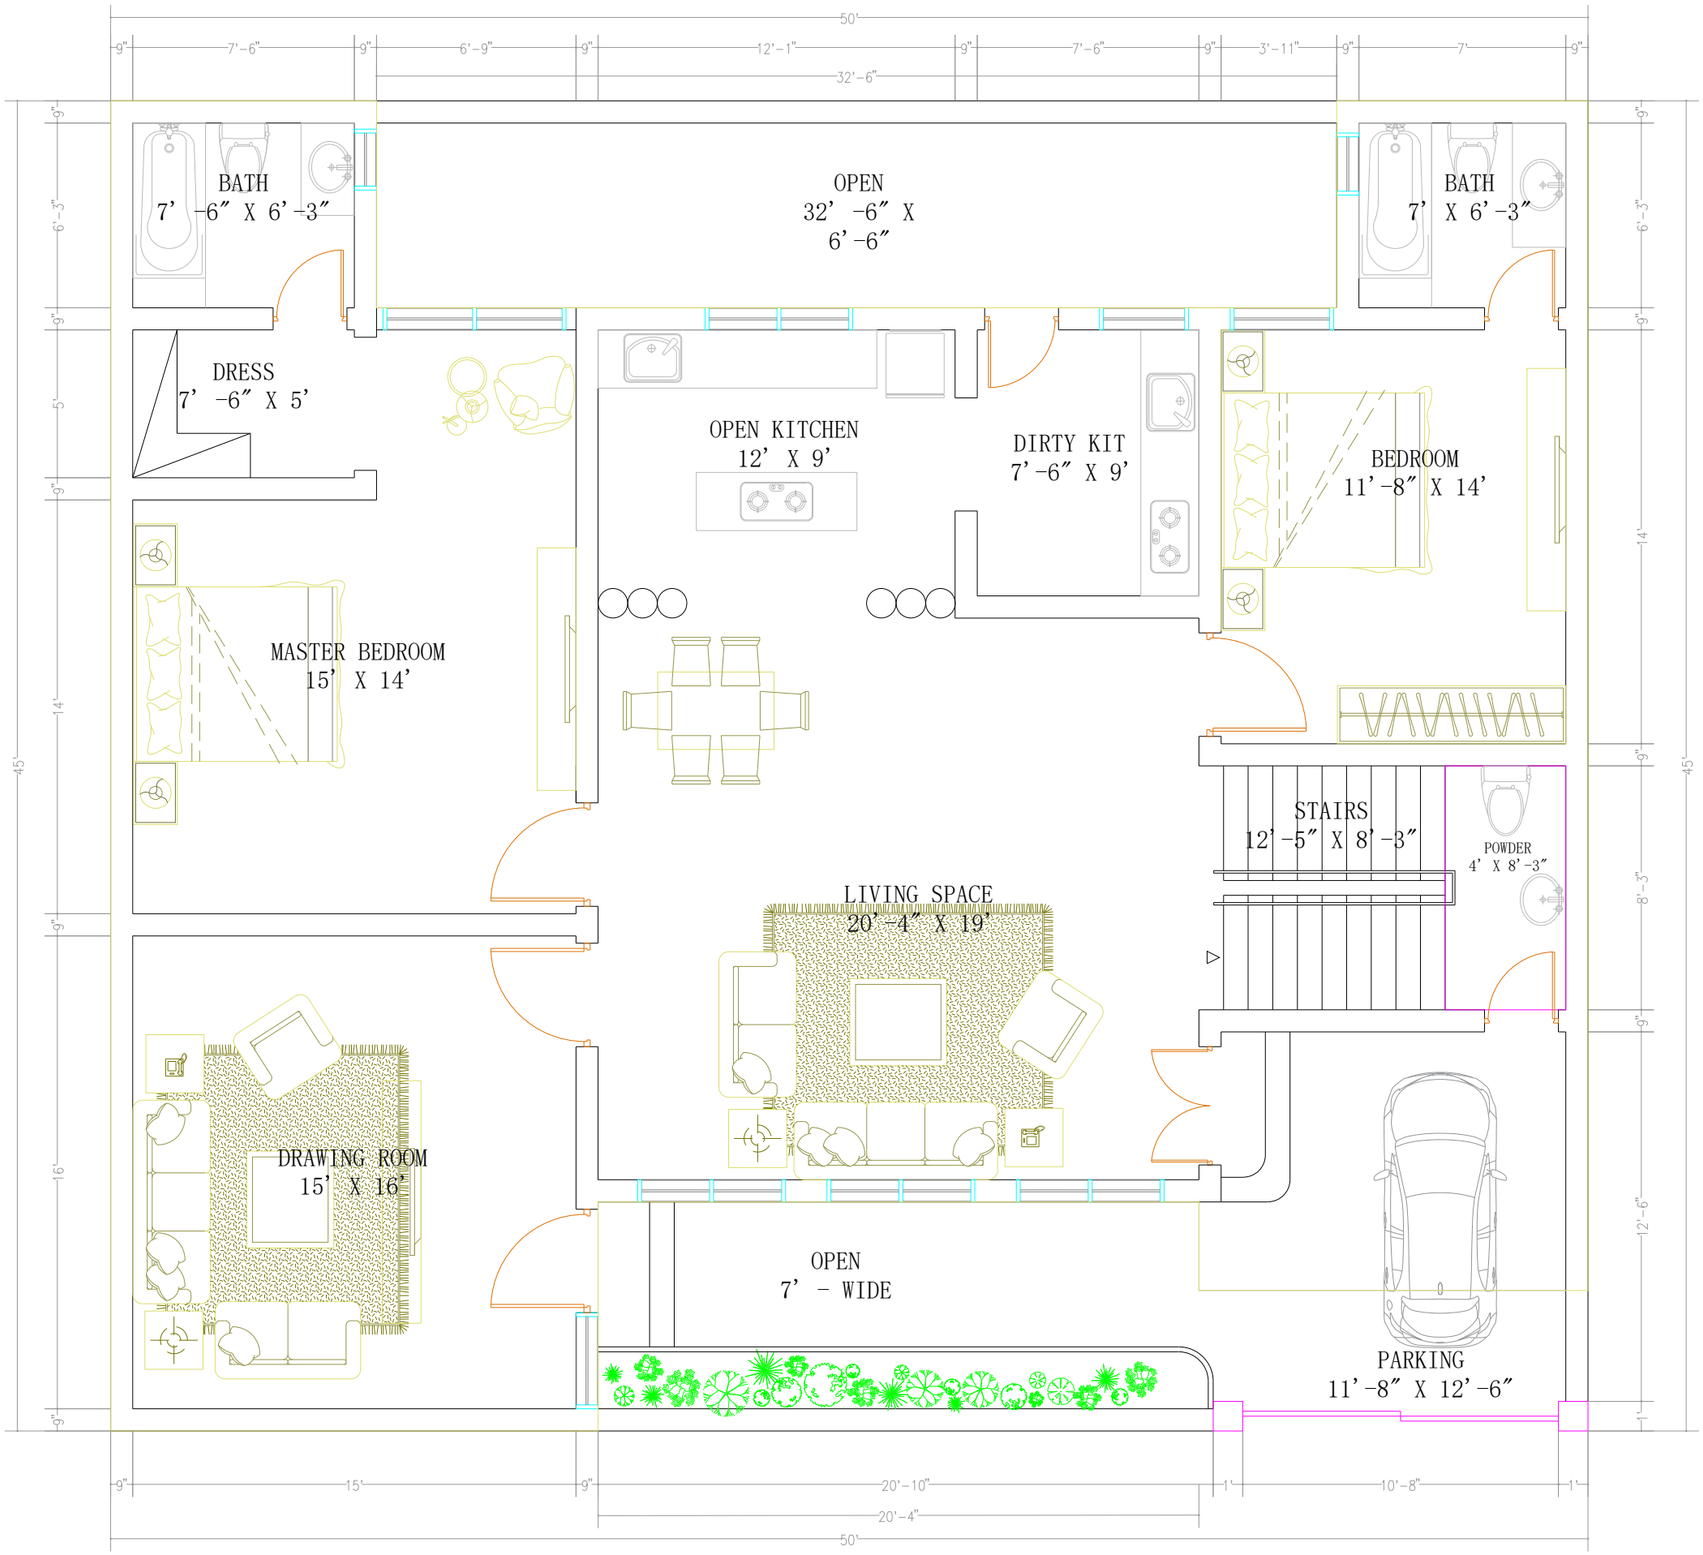



SCHEDULE OF OPENINGS

NO	SIZE	SILL	DESCRIPTION
D	4'-6"x9'-0"	0'-0"	DOUBLE LEAF WOODEN DOOR
D1	3'-6"x7'-6"	0'-0"	WOODEN DOOR
D2	2'-6"x7'-6"	0'-0"	WOODEN DOOR
D3	3'-0"x7'-6"	0'-0"	WOODEN DOOR
W1	8'-0"x6'-0"	1'-6"	ALUMINUM SLIDING WINDOW
W2	7'-0"x6'-0"	1'-6"	ALUMINUM SLIDING WINDOW
W3	6'-0"x4'-6"	3'-0"	ALUMINUM SLIDING WINDOW
W4	4'-6"x6'-6"	1'-0"	ALUMINUM OPENABLE WINDOW
W5	1'-6"x9'-0"	2'-0"	ALUMINUM FIXED GLASS WINDOW
W6	5'-0"x6'-6"	1'-0"	ALUMINUM OPENABLE WINDOW
W7	3'-6"x4'-6"	3'-0"	ALUMINUM SLIDING WINDOW
W8	10'-0"x7'-6"	1'-6"	ALUMINUM SLIDING WINDOW
V1	2'-0"x3'-0"	4'-6"	ALUMINUM SLODING VENTILATOR

CONSULTANT:

PLANIT
ARCHITECTURE AND CONSTRUCTION
03142027726

PROJECT TITTLE:	10 MARLA HOUSE PLAN		
OWNER NAME:	Tahir shah		
LOCATION:	XYZ		
PLOT NO:	XYZ	BLOCK NO:	XYZ
DESIGN BY:	AMIR HASSAN	PROJECT NO:	1093
DRAWN BY:	AMIR HASSAN	SHEET NO:	01
CHECKED BY:	AMIR HASSAN	SHEET SCALE:	1:1
DRAWING TITTLE:	GROUND FLOOR PLAN		

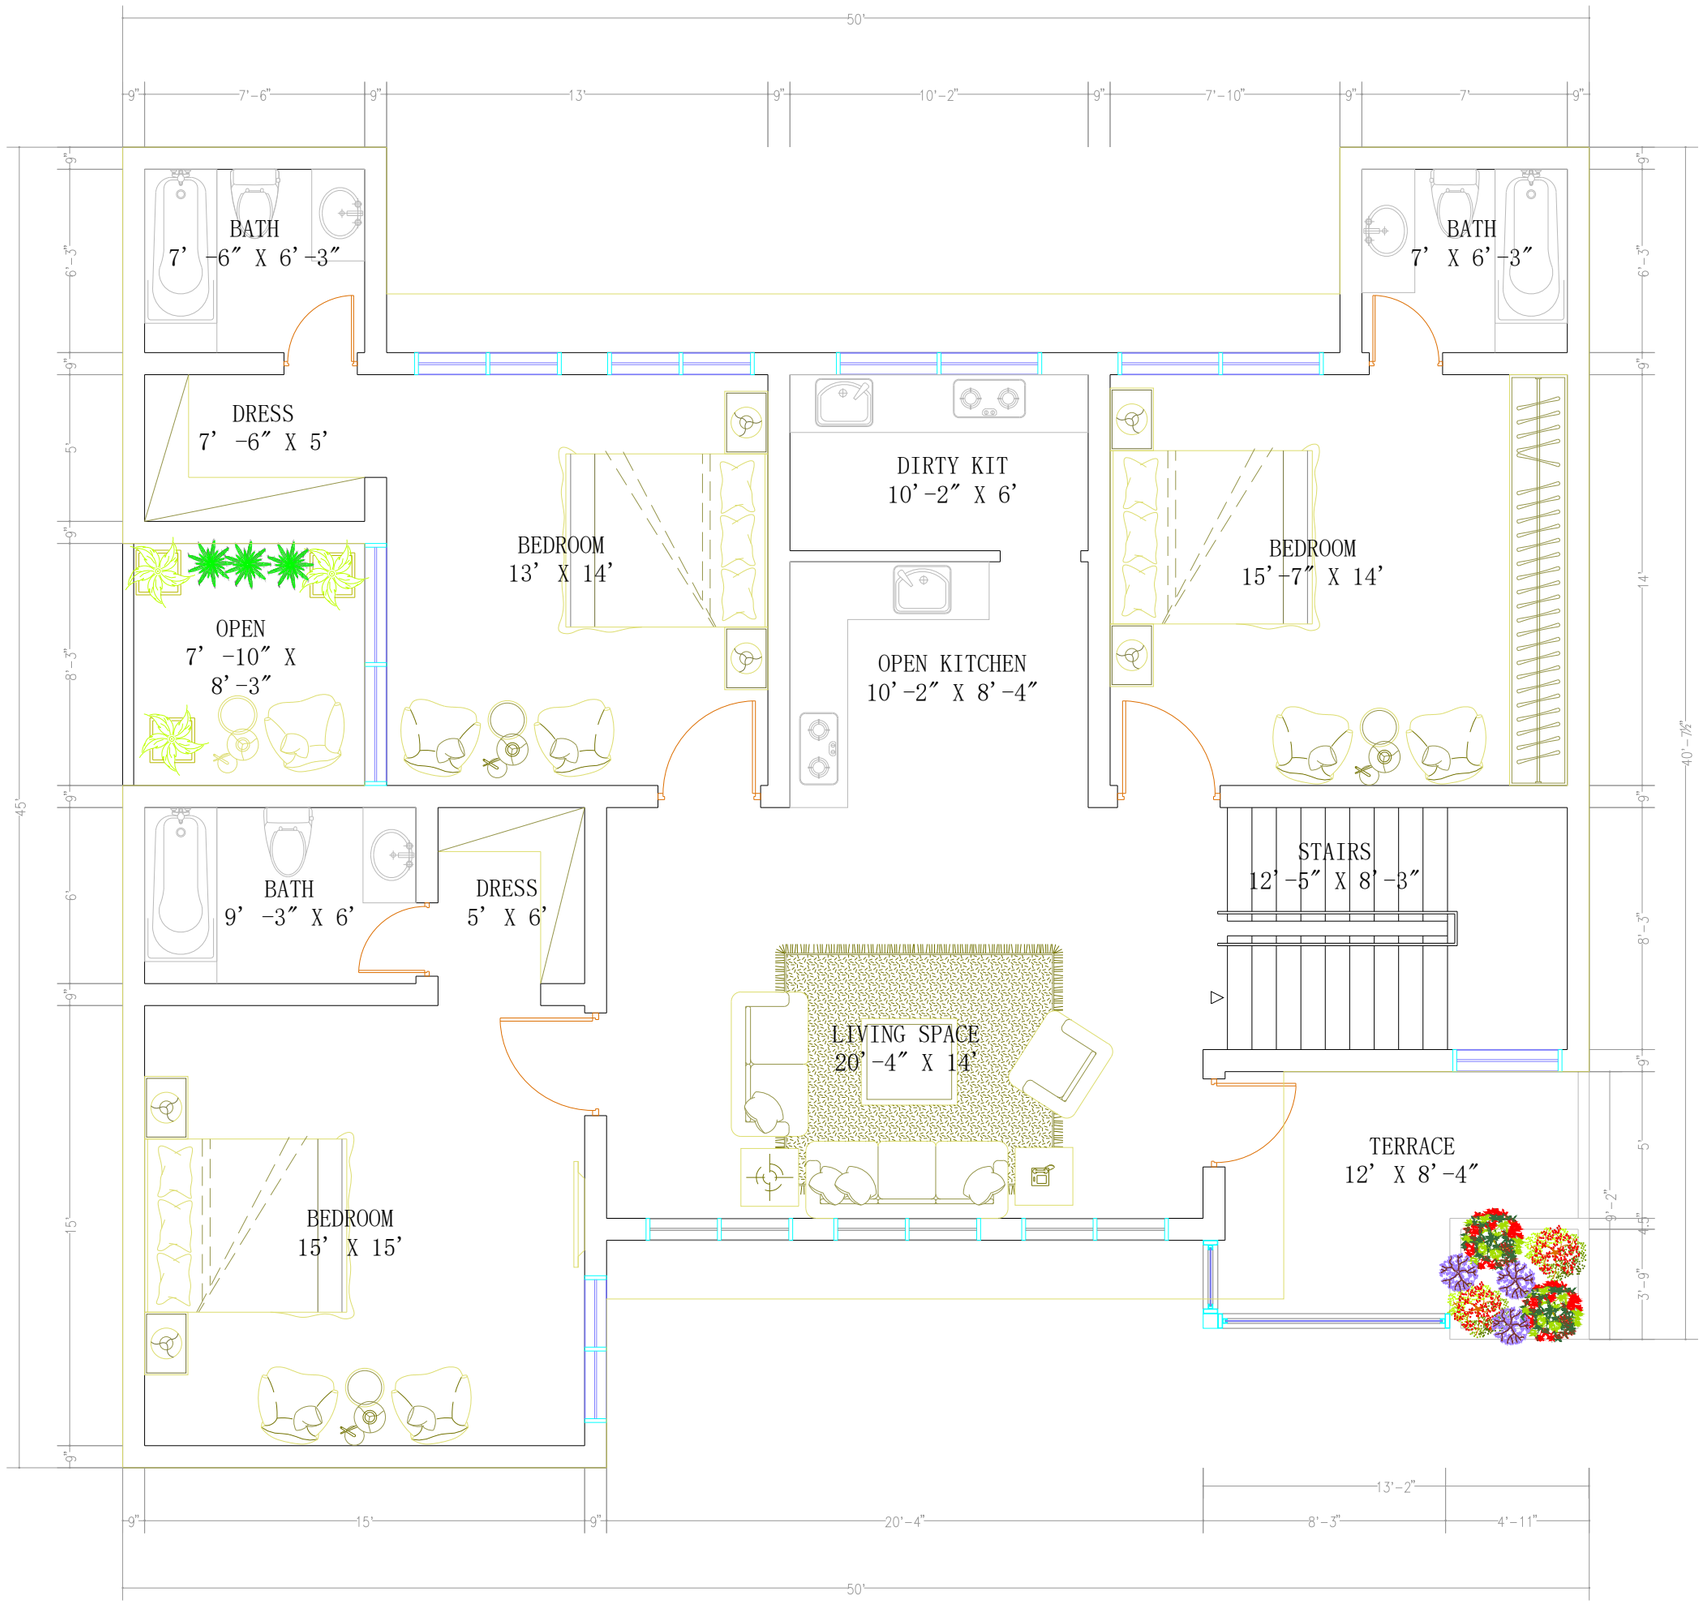

SCHEDULE OF OPENINGS

NO	SIZE	SILL	DESCRIPTION
D	4'-6"x9'-0"	0'-0"	DOUBLE LEAF WOODEN DOOR
D1	3'-6"x7'-6"	0'-0"	WOODEN DOOR
D2	2'-6"x7'-6"	0'-0"	WOODEN DOOR
D3	3'-0"x7'-6"	0'-0"	WOODEN DOOR
W1	8'-0"x6'-0"	1'-6"	ALUMINUM SLIDING WINDOW
W2	7'-0"x6'-0"	1'-6"	ALUMINUM SLIDING WINDOW
W3	6'-0"x4'-6"	3'-0"	ALUMINUM SLIDING WINDOW
W4	4'-6"x6'-6"	1'-0"	ALUMINUM OPENABLE WINDOW
W5	1'-6"x9'-0"	2'-0"	ALUMINUM FIXED GLASS WINDOW
W6	5'-0"x6'-6"	1'-0"	ALUMINUM OPENABLE WINDOW
W7	3'-6"x4'-6"	3'-0"	ALUMINUM SLIDING WINDOW
W8	10'-0"x7'-6"	1'-6"	ALUMINUM SLIDING WINDOW
V1	2'-0"x3'-0"	4'-6"	ALUMINUM SLODING VENTILATOR


CONSULTANT:

PLANIT

ARCHITECTURE AND CONSTRUCTION

03142027726

PROJECT TITTLE:	10 MARLA HOUSE PLAN		
OWNER NAME:	Tahir Shah		
LOCATION:	XYZ		
PLOT NO:	XYZ	BLOCK NO:	XYZ
DESIGN BY:	AMIR HASSAN	PROJECT NO:	1091
DRAWN BY:	AMIR HASSAN	SHEET NO:	01
CHECKED BY:	AMIR HASSAN	SHEET SCALE:	1:1
DRAWING TITTLE:	FIRST FLOOR PLAN		

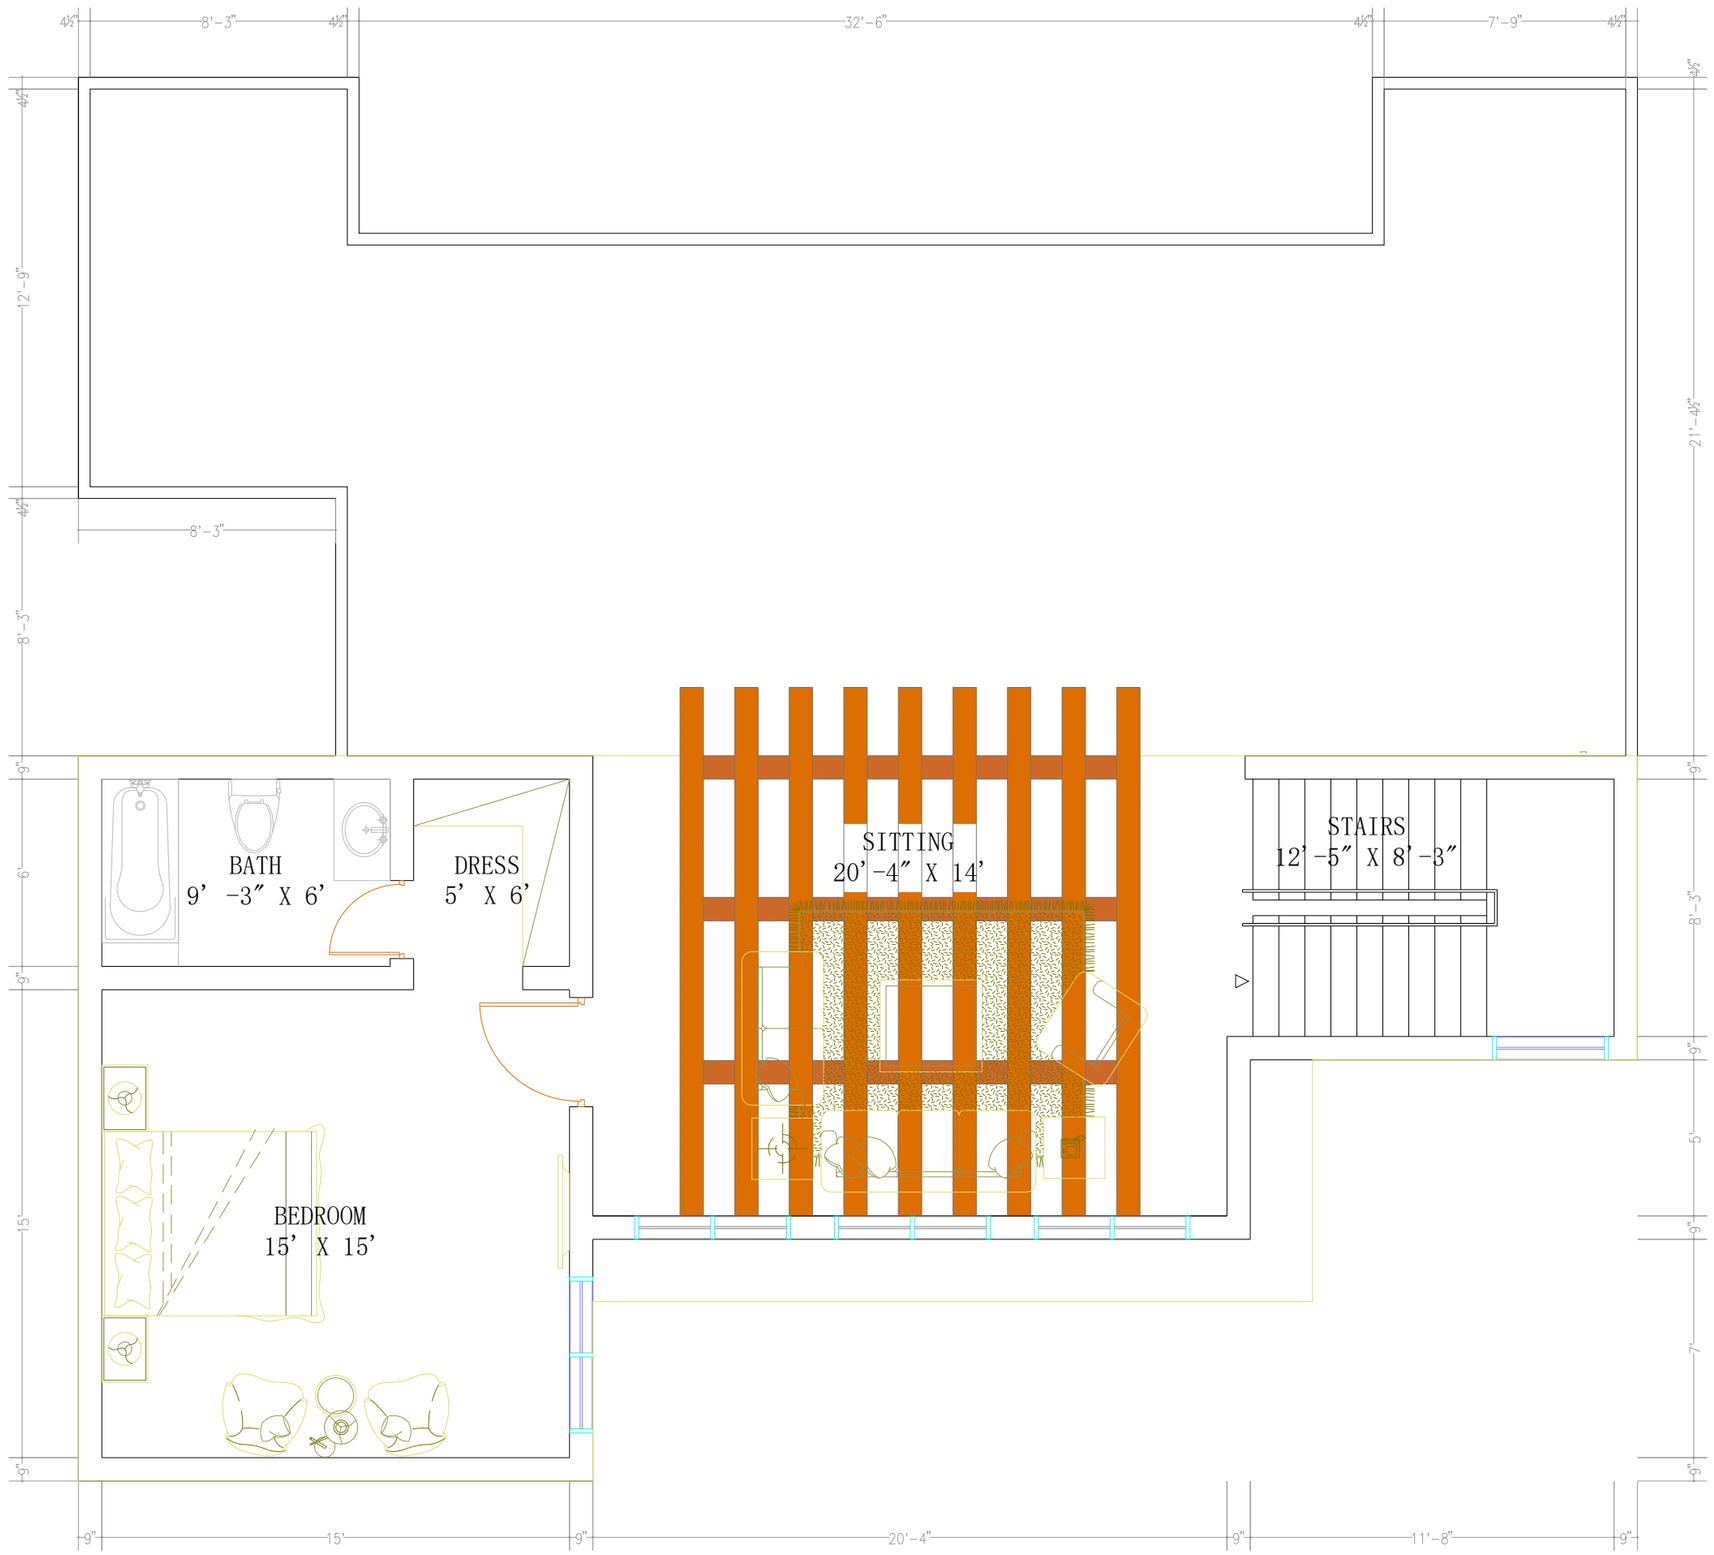

SCHEDULE OF OPENINGS

NO	SIZE	SILL	DESCRIPTION
D	4'-6"x9'-0"	0'-0"	DOUBLE LEAF WOODEN DOOR
D1	3'-6"x7'-6"	0'-0"	WOODEN DOOR
D2	2'-6"x7'-6"	0'-0"	WOODEN DOOR
D3	3'-0"x7'-6"	0'-0"	WOODEN DOOR
W1	8'-0"x6'-0"	1'-6"	ALUMINUM SLIDING WINDOW
W2	7'-0"x6'-0"	1'-6"	ALUMINUM SLIDING WINDOW
W3	6'-0"x4'-6"	3'-0"	ALUMINUM SLIDING WINDOW
W4	4'-6"x6'-6"	1'-0"	ALUMINUM OPENABLE WINDOW
W5	1'-6"x9'-0"	2'-0"	ALUMINUM FIXED GLASS WINDOW
W6	5'-0"x6'-6"	1'-0"	ALUMINUM OPENABLE WINDOW
W7	3'-6"x4'-6"	3'-0"	ALUMINUM SLIDING WINDOW
W8	10'-0"x7'-6"	1'-6"	ALUMINUM SLIDING WINDOW
V1	2'-0"x3'-0"	4'-6"	ALUMINUM SLODING VENTILATOR

CONSULTANT:

PLANIT
ARCHITECTURE AND CONSTRUCTION
03142027726

PROJECT TITTLE:	10 MARLA HOUSE PLAN		
OWNER NAME:	Tahir Shah		
LOCATION:	XYZ		
PLOT NO:	XYZ	BLOCK NO:	XYZ
DESIGN BY:	AMIR HASSAN	PROJECT NO:	1091
DRAWN BY:	AMIR HASSAN	SHEET NO:	01
CHECKED BY:	AMIR HASSAN	SHEET SCALE:	1:1
DRAWING TITTLE:	MUMMTI PLAN		