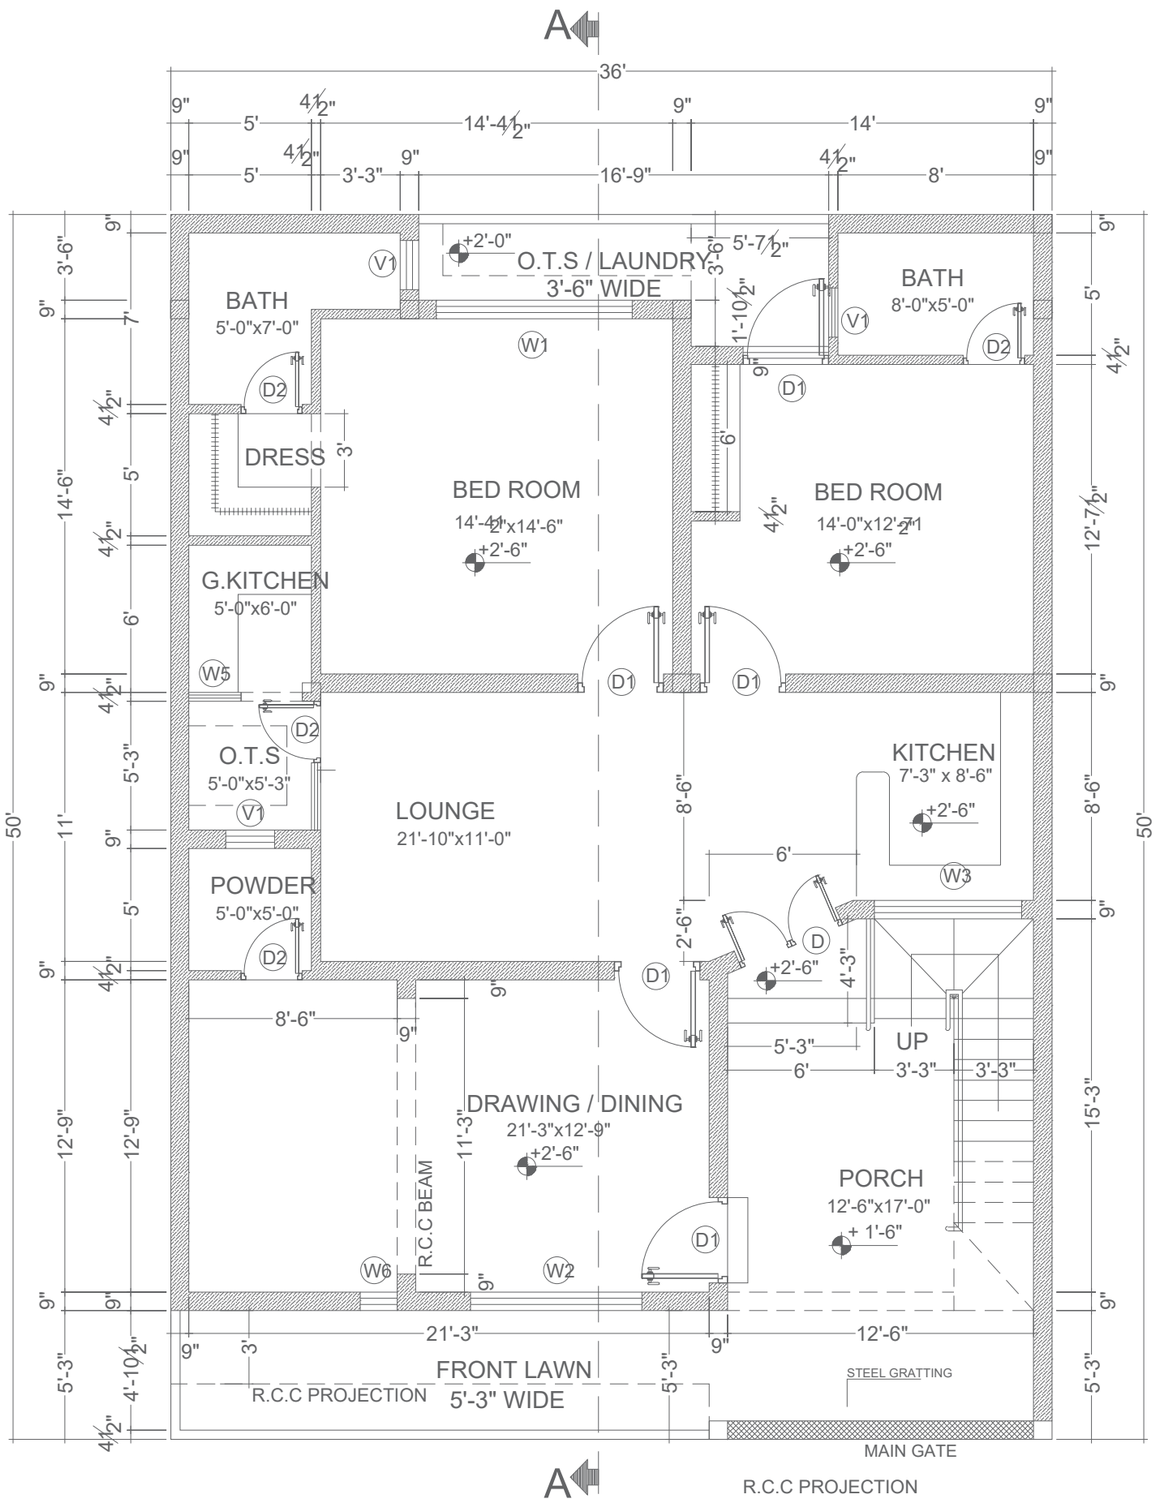



# GROUND FLOOR PLAN

± 0'-0"


## SCHEDULE OF OPENINGS

| NO | SIZE | SILL | DESCRIPTION |
|---|---|---|---|
| D | 4'-6"x9'-0" | 0'-0" | DOUBLE LEAF WOODEN DOOR |
| D1 | 3'-6"x7'-6" | 0'-0" | WOODEN DOOR |
| D2 | 2'-6"x7'-6" | 0'-0" | WOODEN DOOR |
| D3 | 3'-0"x7'-6" | 0'-0" | WOODEN DOOR |
| | | | |
| W1 | 8'-0"x6'-0" | 1'-6" | ALUMINUM SLIDING WINDOW |
| W2 | 7'-0"x6'-0" | 1'-6" | ALUMINUM SLIDING WINDOW |
| W3 | 6'-0"x4'-6" | 3'-0" | ALUMINUM SLIDING WINDOW |
| W4 | 4'-6"x6'-6" | 1'-0" | ALUMINUM OPENABLE WINDOW |
| W5 | 1'-6"x9'-0" | 2'-0" | ALUMINUM FIXED GLASS WINDOW |
| W6 | 5'-0"x6'-6" | 1'-0" | ALUMINUM OPENABLE WINDOW |
| W7 | 3'-6"x4'-6" | 3'-0" | ALUMINUM SLIDING WINDOW |
| W8 | 10'-0"x7'-6" | 1'-6" | ALUMINUM SLIDING WINDOW |
| V1 | 2'-0"x3'-0" | 4'-6" | ALUMINUM SLODING VENTILATOR |

CONSULTANT:

PLANIT
ARCHITECTURE AND CONSTRUCTION
03142027726

| | | | |
|---|---|---|---|
| PROJECT TITTLE: | 08 MARLA HOUSE PLAN | | |
| OWNER NAME: | XYZ | | |
| LOCATION: | XYZ | | |
| PLOT NO: | XYZ | BLOCK NO: | XYZ |
| DESIGN BY: | AMIR HASSAN | PROJECT NO: | 1091 |
| DRAWN BY: | AMIR HASSAN | SHEET NO: | 02 |
| CHECKED BY: | AMIR HASSAN | SHEET SCALE: | 1:1 |
| DRAWING TITTLE: | GROUND FLOOR PLAN | | |

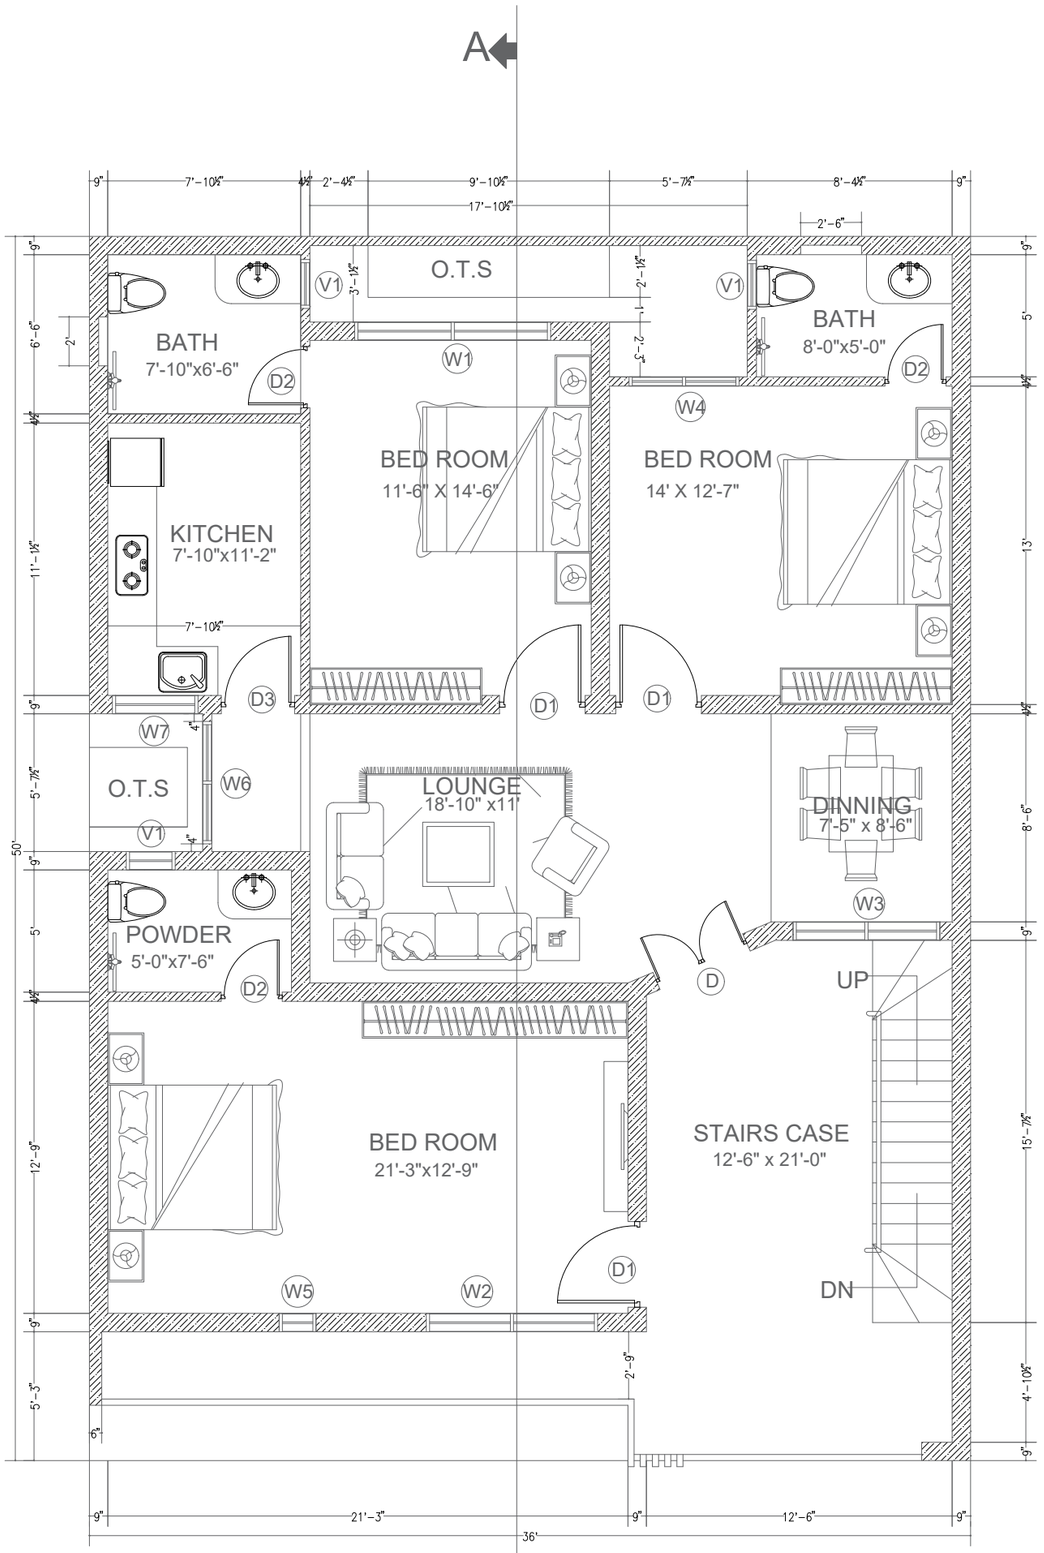


FIRST FLOOR PLAN A


## SCHEDULE OF OPENINGS

| NO | SIZE | SILL | DESCRIPTION |
|---|---|---|---|
| D | 4'-6"x9'-0" | 0'-0" | DOUBLE LEAF WOODEN DOOR |
| D1 | 3'-6"x7'-6" | 0'-0" | WOODEN DOOR |
| D2 | 2'-6"x7'-6" | 0'-0" | WOODEN DOOR |
| D3 | 3'-0"x7'-6" | 0'-0" | WOODEN DOOR |
| | | | |
| W1 | 8'-0"x6'-0" | 1'-6" | ALUMINUM SLIDING WINDOW |
| W2 | 7'-0"x6'-0" | 1'-6" | ALUMINUM SLIDING WINDOW |
| W3 | 6'-0"x4'-6" | 3'-0" | ALUMINUM SLIDING WINDOW |
| W4 | 4'-6"x6'-6" | 1'-0" | ALUMINUM OPENABLE WINDOW |
| W5 | 1'-6"x9'-0" | 2'-0" | ALUMINUM FIXED GLASS WINDOW |
| W6 | 5'-0"x6'-6" | 1'-0" | ALUMINUM OPENABLE WINDOW |
| W7 | 3'-6"x4'-6" | 3'-0" | ALUMINUM SLIDING WINDOW |
| W8 | 10'-0"x7'-6" | 1'-6" | ALUMINUM SLIDING WINDOW |
| V1 | 2'-0"x3'-0" | 4'-6" | ALUMINUM SLODING VENTILATOR |

CONSULTANT:

PLANIT
ARCHITECTURE AND CONSTRUCTION
03142027726

| | | | |
|---|---|---|---|
| PROJECT TITTLE: | 08 MARLA HOUSE PLAN | | |
| OWNER NAME: | XYZ | | |
| LOCATION: | XYZ | | |
| PLOT NO: | XYZ | BLOCK NO: | XYZ |
| DESIGN BY: | AMIR HASSAN | PROJECT NO: | 1091 |
| DRAWN BY: | AMIR HASSAN | SHEET NO: | 02 |
| CHECKED BY: | AMIR HASSAN | SHEET SCALE: | 1:1 |
| DRAWING TITTLE: | FIRST FLOOR PLAN | | |

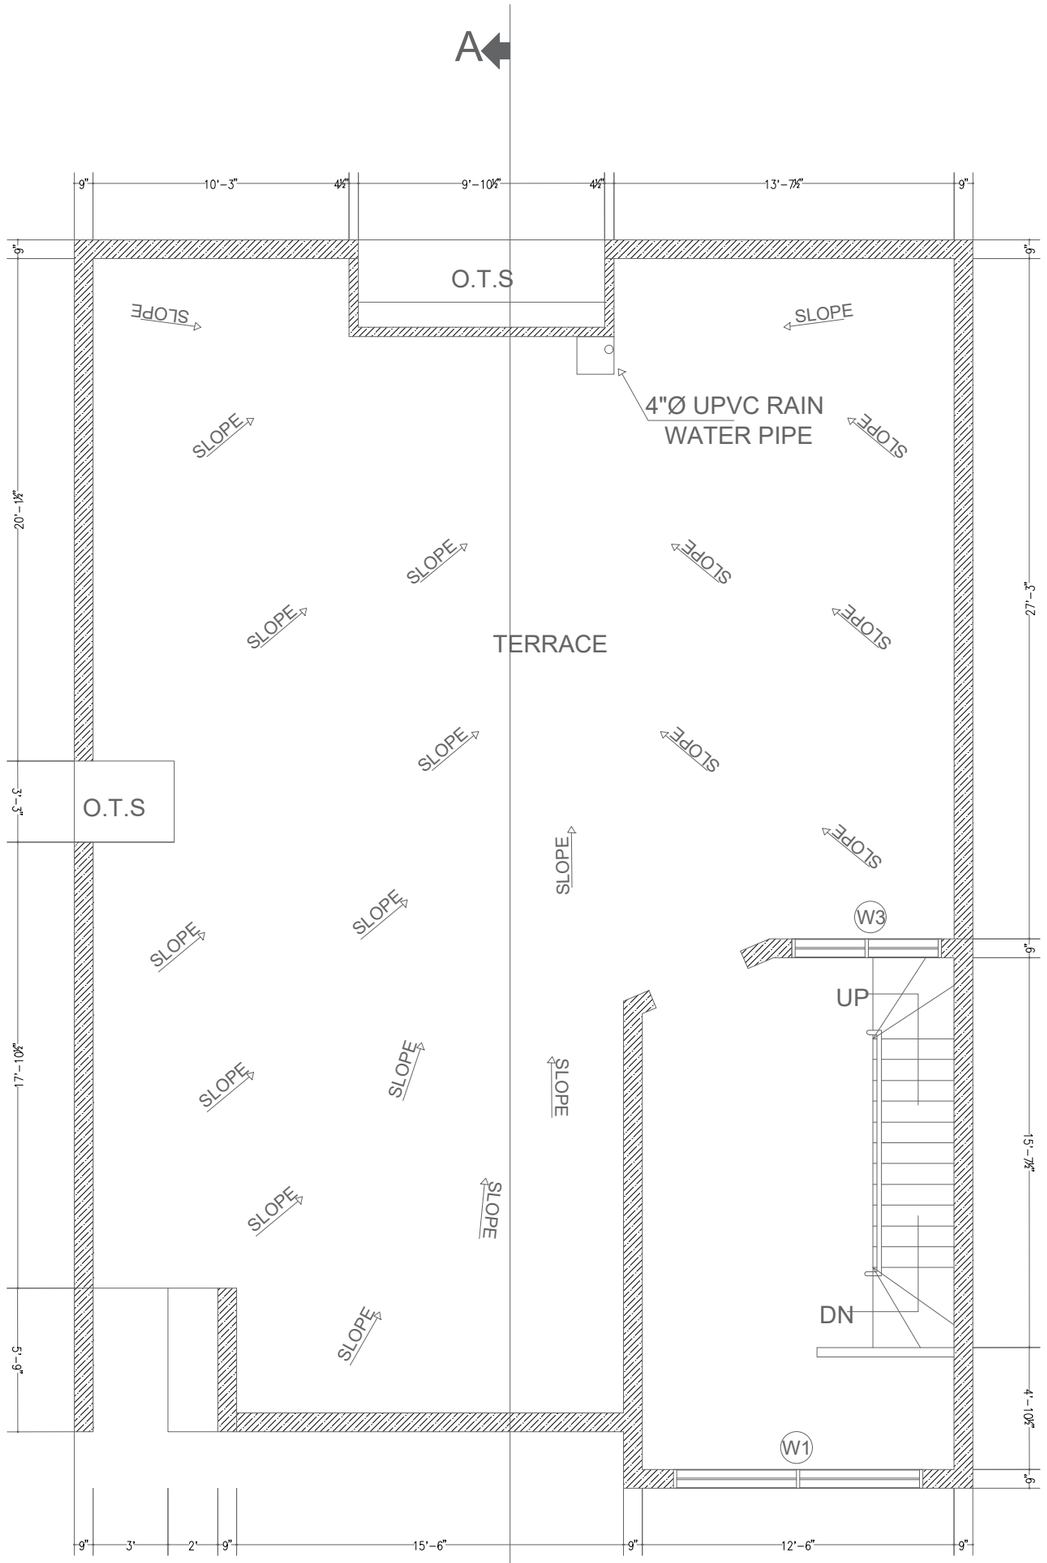


MUMTY PLAN

ARCHITECTURE DETAILS


## SCHEDULE OF OPENINGS

| NO | SIZE | SILL | DESCRIPTION |
|---|---|---|---|
| D | 4'-6"x9'-0" | 0'-0" | DOUBLE LEAF WOODEN DOOR |
| D1 | 3'-6"x7'-6" | 0'-0" | WOODEN DOOR |
| D2 | 2'-6"x7'-6" | 0'-0" | WOODEN DOOR |
| D3 | 3'-0"x7'-6" | 0'-0" | WOODEN DOOR |
| | | | |
| W1 | 8'-0"x6'-0" | 1'-6" | ALUMINUM SLIDING WINDOW |
| W2 | 7'-0"x6'-0" | 1'-6" | ALUMINUM SLIDING WINDOW |
| W3 | 6'-0"x4'-6" | 3'-0" | ALUMINUM SLIDING WINDOW |
| W4 | 4'-6"x6'-6" | 1'-0" | ALUMINUM OPENABLE WINDOW |
| W5 | 1'-6"x9'-0" | 2'-0" | ALUMINUM FIXED GLASS WINDOW |
| W6 | 5'-0"x6'-6" | 1'-0" | ALUMINUM OPENABLE WINDOW |
| W7 | 3'-6"x4'-6" | 3'-0" | ALUMINUM SLIDING WINDOW |
| W8 | 10'-0"x7'-6" | 1'-6" | ALUMINUM SLIDING WINDOW |
| V1 | 2'-0"x3'-0" | 4'-6" | ALUMINUM SLODING VENTILATOR |

CONSULTANT:

PLANIT
ARCHITECTURE AND CONSTRUCTION
03142027726

| | | | |
|---|---|---|---|
| PROJECT TITTLE: | 08 MARLA HOUSE PLAN | | |
| OWNER NAME: | XYZ | | |
| LOCATION: | XYZ | | |
| PLOT NO: | XYZ | BLOCK NO: | XYZ |
| DESIGN BY: | AMIR HASSAN | PROJECT NO: | 1091 |
| DRAWN BY: | AMIR HASSAN | SHEET NO: | 01 |
| CHECKED BY: | AMIR HASSAN | SHEET SCALE: | 1:1 |
| DRAWING TITTLE: | MUMMTI PLAN | | |

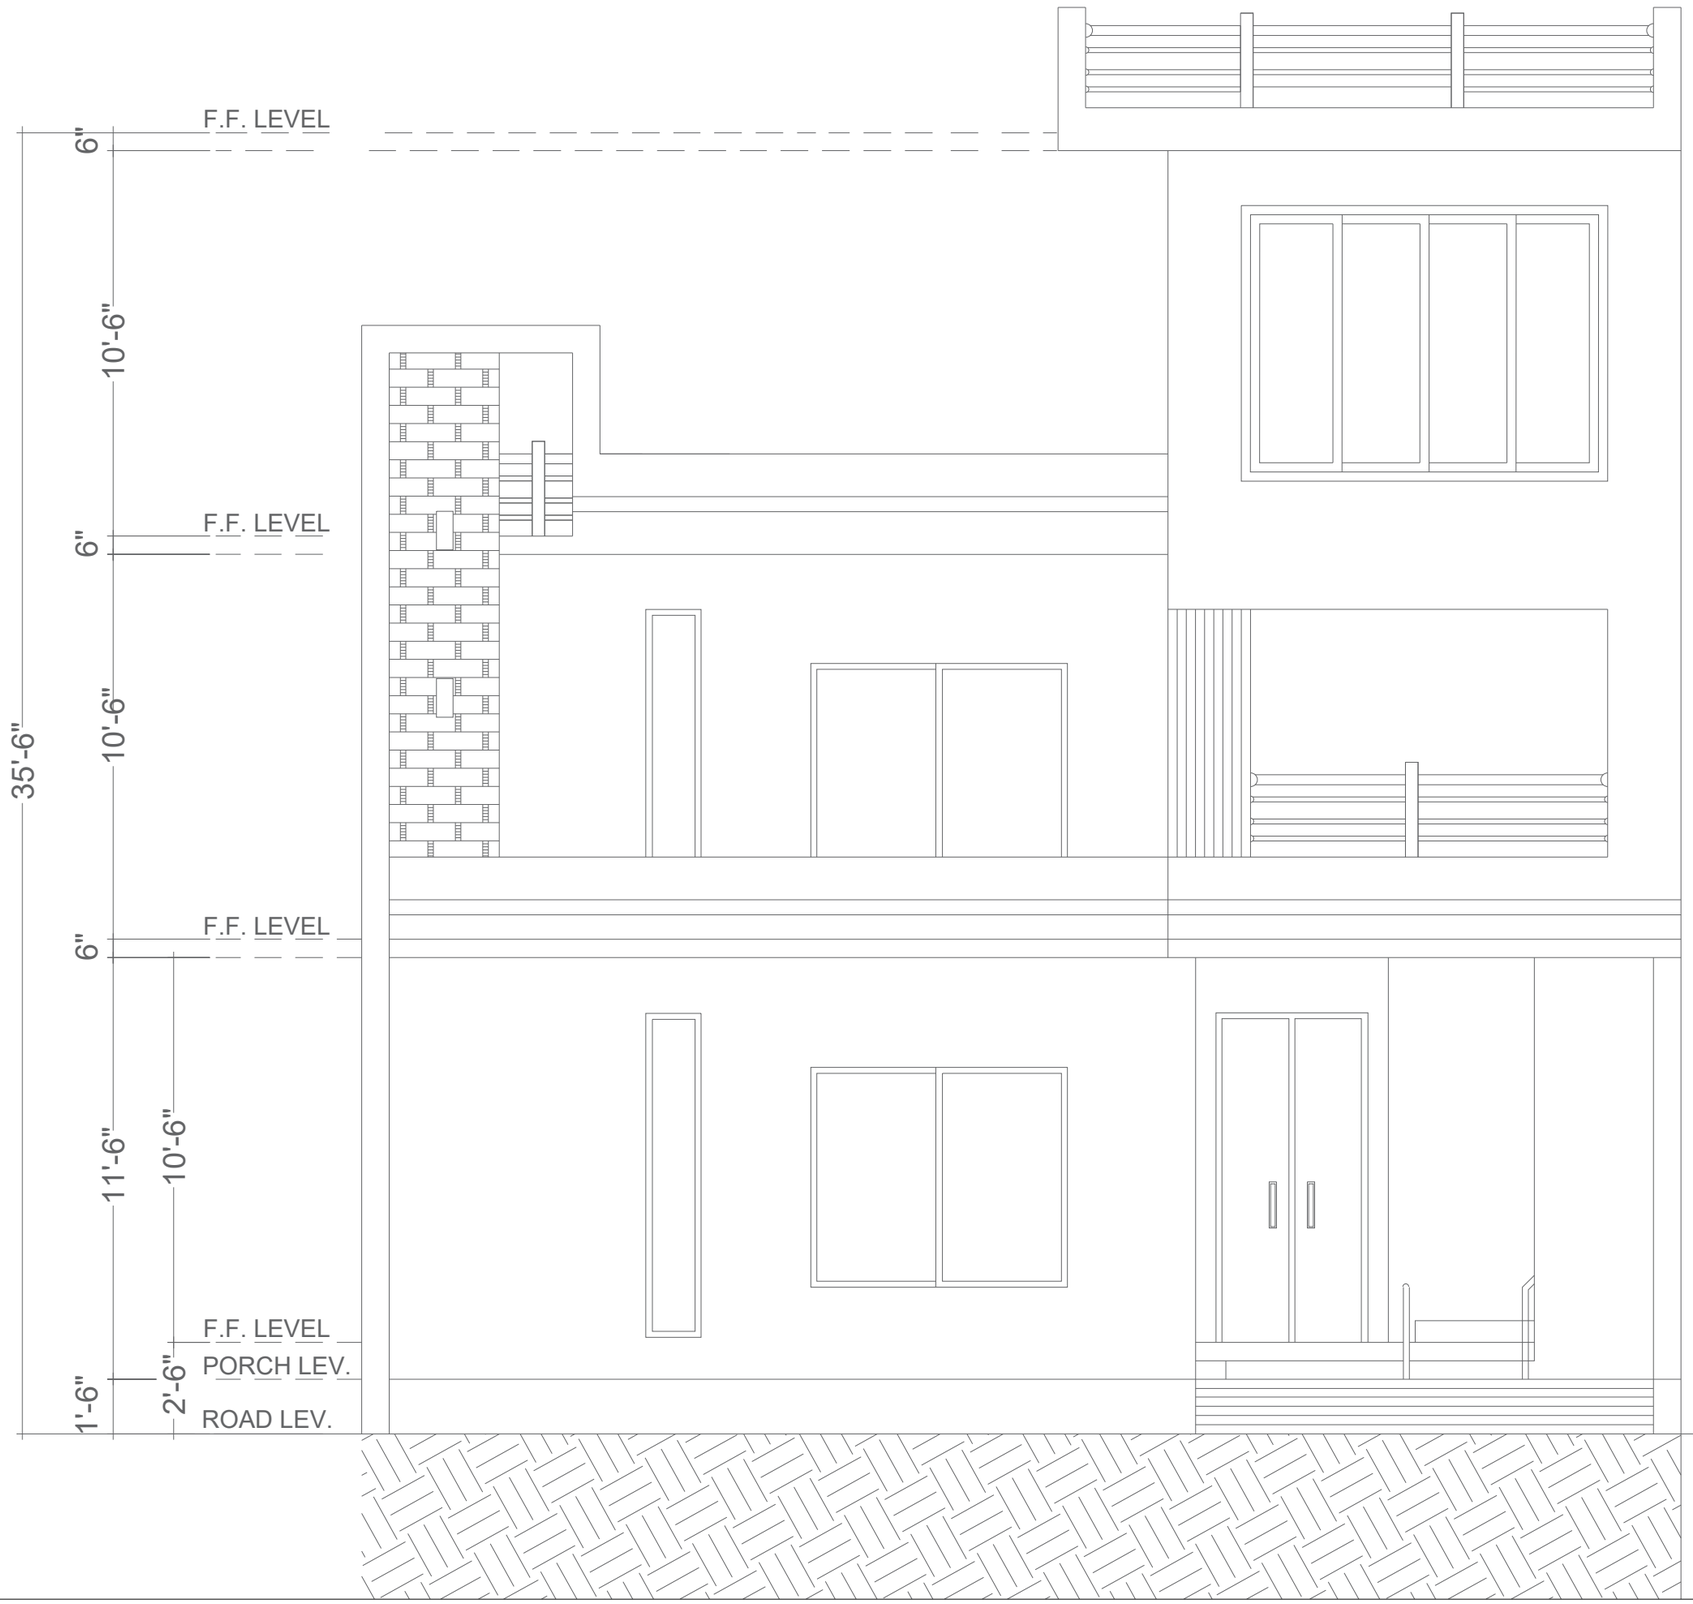


ARCHITECTURE DETAILS


## SCHEDULE OF OPENINGS

| NO | SIZE | SILL | DESCRIPTION |
|---|---|---|---|
| D | 4'-6"x9'-0" | 0'-0" | DOUBLE LEAF WOODEN DOOR |
| D1 | 3'-6"x7'-6" | 0'-0" | WOODEN DOOR |
| D2 | 2'-6"x7'-6" | 0'-0" | WOODEN DOOR |
| D3 | 3'-0"x7'-6" | 0'-0" | WOODEN DOOR |
| | | | |
| W1 | 8'-0"x6'-0" | 1'-6" | ALUMINUM SLIDING WINDOW |
| W2 | 7'-0"x6'-0" | 1'-6" | ALUMINUM SLIDING WINDOW |
| W3 | 6'-0"x4'-6" | 3'-0" | ALUMINUM SLIDING WINDOW |
| W4 | 4'-6"x6'-6" | 1'-0" | ALUMINUM OPENABLE WINDOW |
| W5 | 1'-6"x9'-0" | 2'-0" | ALUMINUM FIXED GLASS WINDOW |
| W6 | 5'-0"x6'-6" | 1'-0" | ALUMINUM OPENABLE WINDOW |
| W7 | 3'-6"x4'-6" | 3'-0" | ALUMINUM SLIDING WINDOW |
| W8 | 10'-0"x7'-6" | 1'-6" | ALUMINUM SLIDING WINDOW |
| V1 | 2'-0"x3'-0" | 4'-6" | ALUMINUM SLODING VENTILATOR |


CONSULTANT:

PLANIT
ARCHITECTURE AND CONSTRUCTION
03142027726

| | | | |
|---|---|---|---|
| PROJECT TITTLE: | 08 MARLA HOUSE PLAN | | |
| OWNER NAME: | XYZ | | |
| LOCATION: | XYZ | | |
| PLOT NO: | XYZ | BLOCK NO: | XYZ |
| DESIGN BY: | AMIR HASSAN | PROJECT NO: | 1091 |
| DRAWN BY: | AMIR HASSAN | SHEET NO: | 01 |
| CHECKED BY: | AMIR HASSAN | SHEET SCALE: | 1:1 |
| DRAWING TITTLE: | MUMMTI PLAN | | |

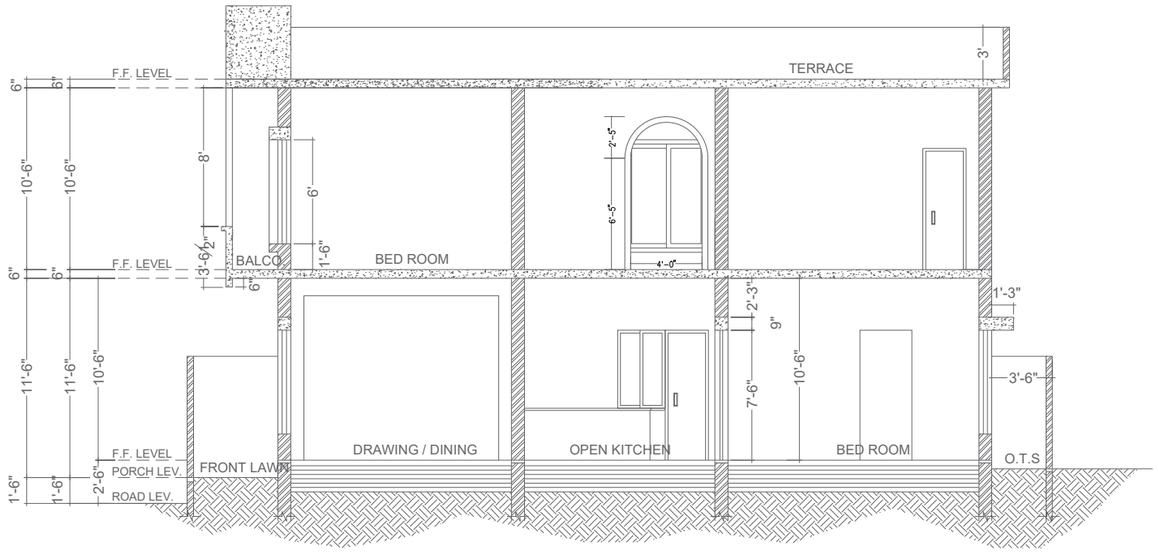


SECTION AT A-A

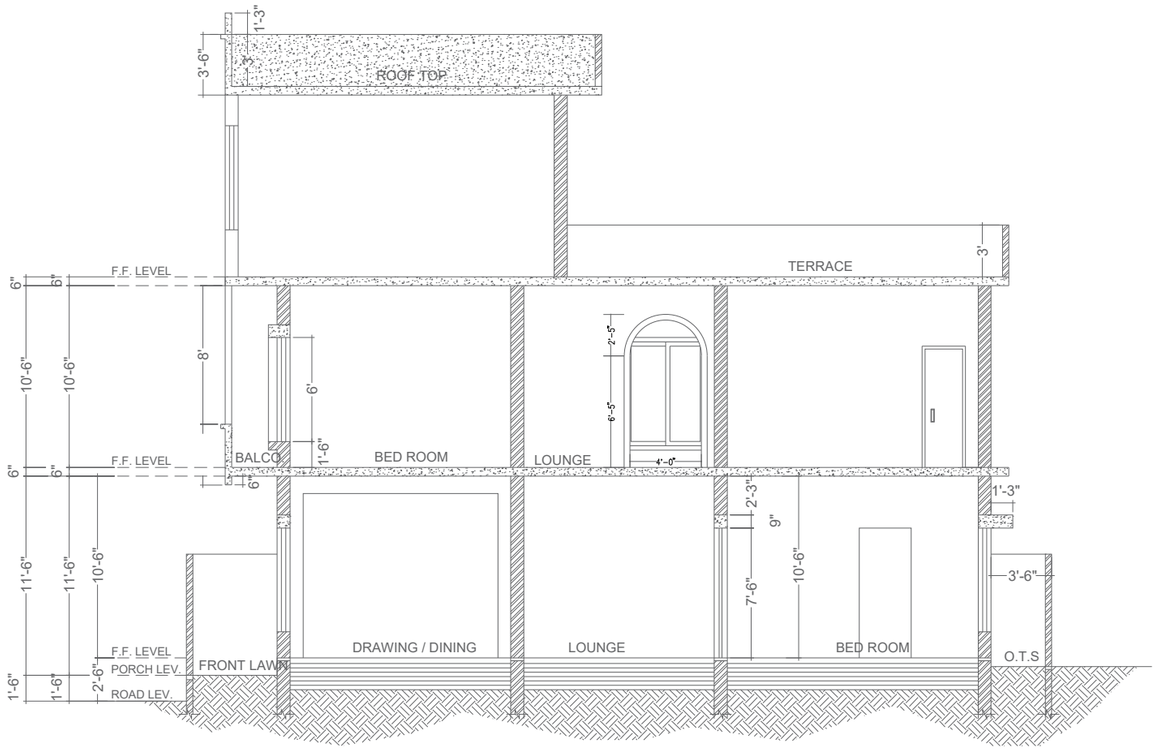


SECTION

ARCHITECTURE DETAILS

## SCHEDULE OF OPENINGS

| NO | SIZE | SILL | DESCRIPTION |
|---|---|---|---|
| D | 4'-6"x9'-0" | 0'-0" | DOUBLE LEAF WOODEN DOOR |
| D1 | 3'-6"x7'-6" | 0'-0" | WOODEN DOOR |
| D2 | 2'-6"x7'-6" | 0'-0" | WOODEN DOOR |
| D3 | 3'-0"x7'-6" | 0'-0" | WOODEN DOOR |
| | | | |
| W1 | 8'-0"x6'-0" | 1'-6" | ALUMINUM SLIDING WINDOW |
| W2 | 7'-0"x6'-0" | 1'-6" | ALUMINUM SLIDING WINDOW |
| W3 | 6'-0"x4'-6" | 3'-0" | ALUMINUM SLIDING WINDOW |
| W4 | 4'-6"x6'-6" | 1'-0" | ALUMINUM OPENABLE WINDOW |
| W5 | 1'-6"x9'-0" | 2'-0" | ALUMINUM FIXED GLASS WINDOW |
| W6 | 5'-0"x6'-6" | 1'-0" | ALUMINUM OPENABLE WINDOW |
| W7 | 3'-6"x4'-6" | 3'-0" | ALUMINUM SLIDING WINDOW |
| W8 | 10'-0"x7'-6" | 1'-6" | ALUMINUM SLIDING WINDOW |
| V1 | 2'-0"x3'-0" | 4'-6" | ALUMINUM SLODING VENTILATOR |

CONSULTANT:

PLANIT
ARCHITECTURE AND CONSTRUCTION
03142027726

| | | | |
|---|---|---|---|
| PROJECT TITTLE: | 08 MARLA HOUSE PLAN | | |
| OWNER NAME: | XYZ | | |
| LOCATION: | XYZ | | |
| PLOT NO: | XYZ | BLOCK NO: | XYZ |
| DESIGN BY: | AMIR HASSAN | PROJECT NO: | 1091 |
| DRAWN BY: | AMIR HASSAN | SHEET NO: | 01 |
| CHECKED BY: | AMIR HASSAN | SHEET SCALE: | 1:1 |
| DRAWING TITTLE: | MUMMTI PLAN | | |